


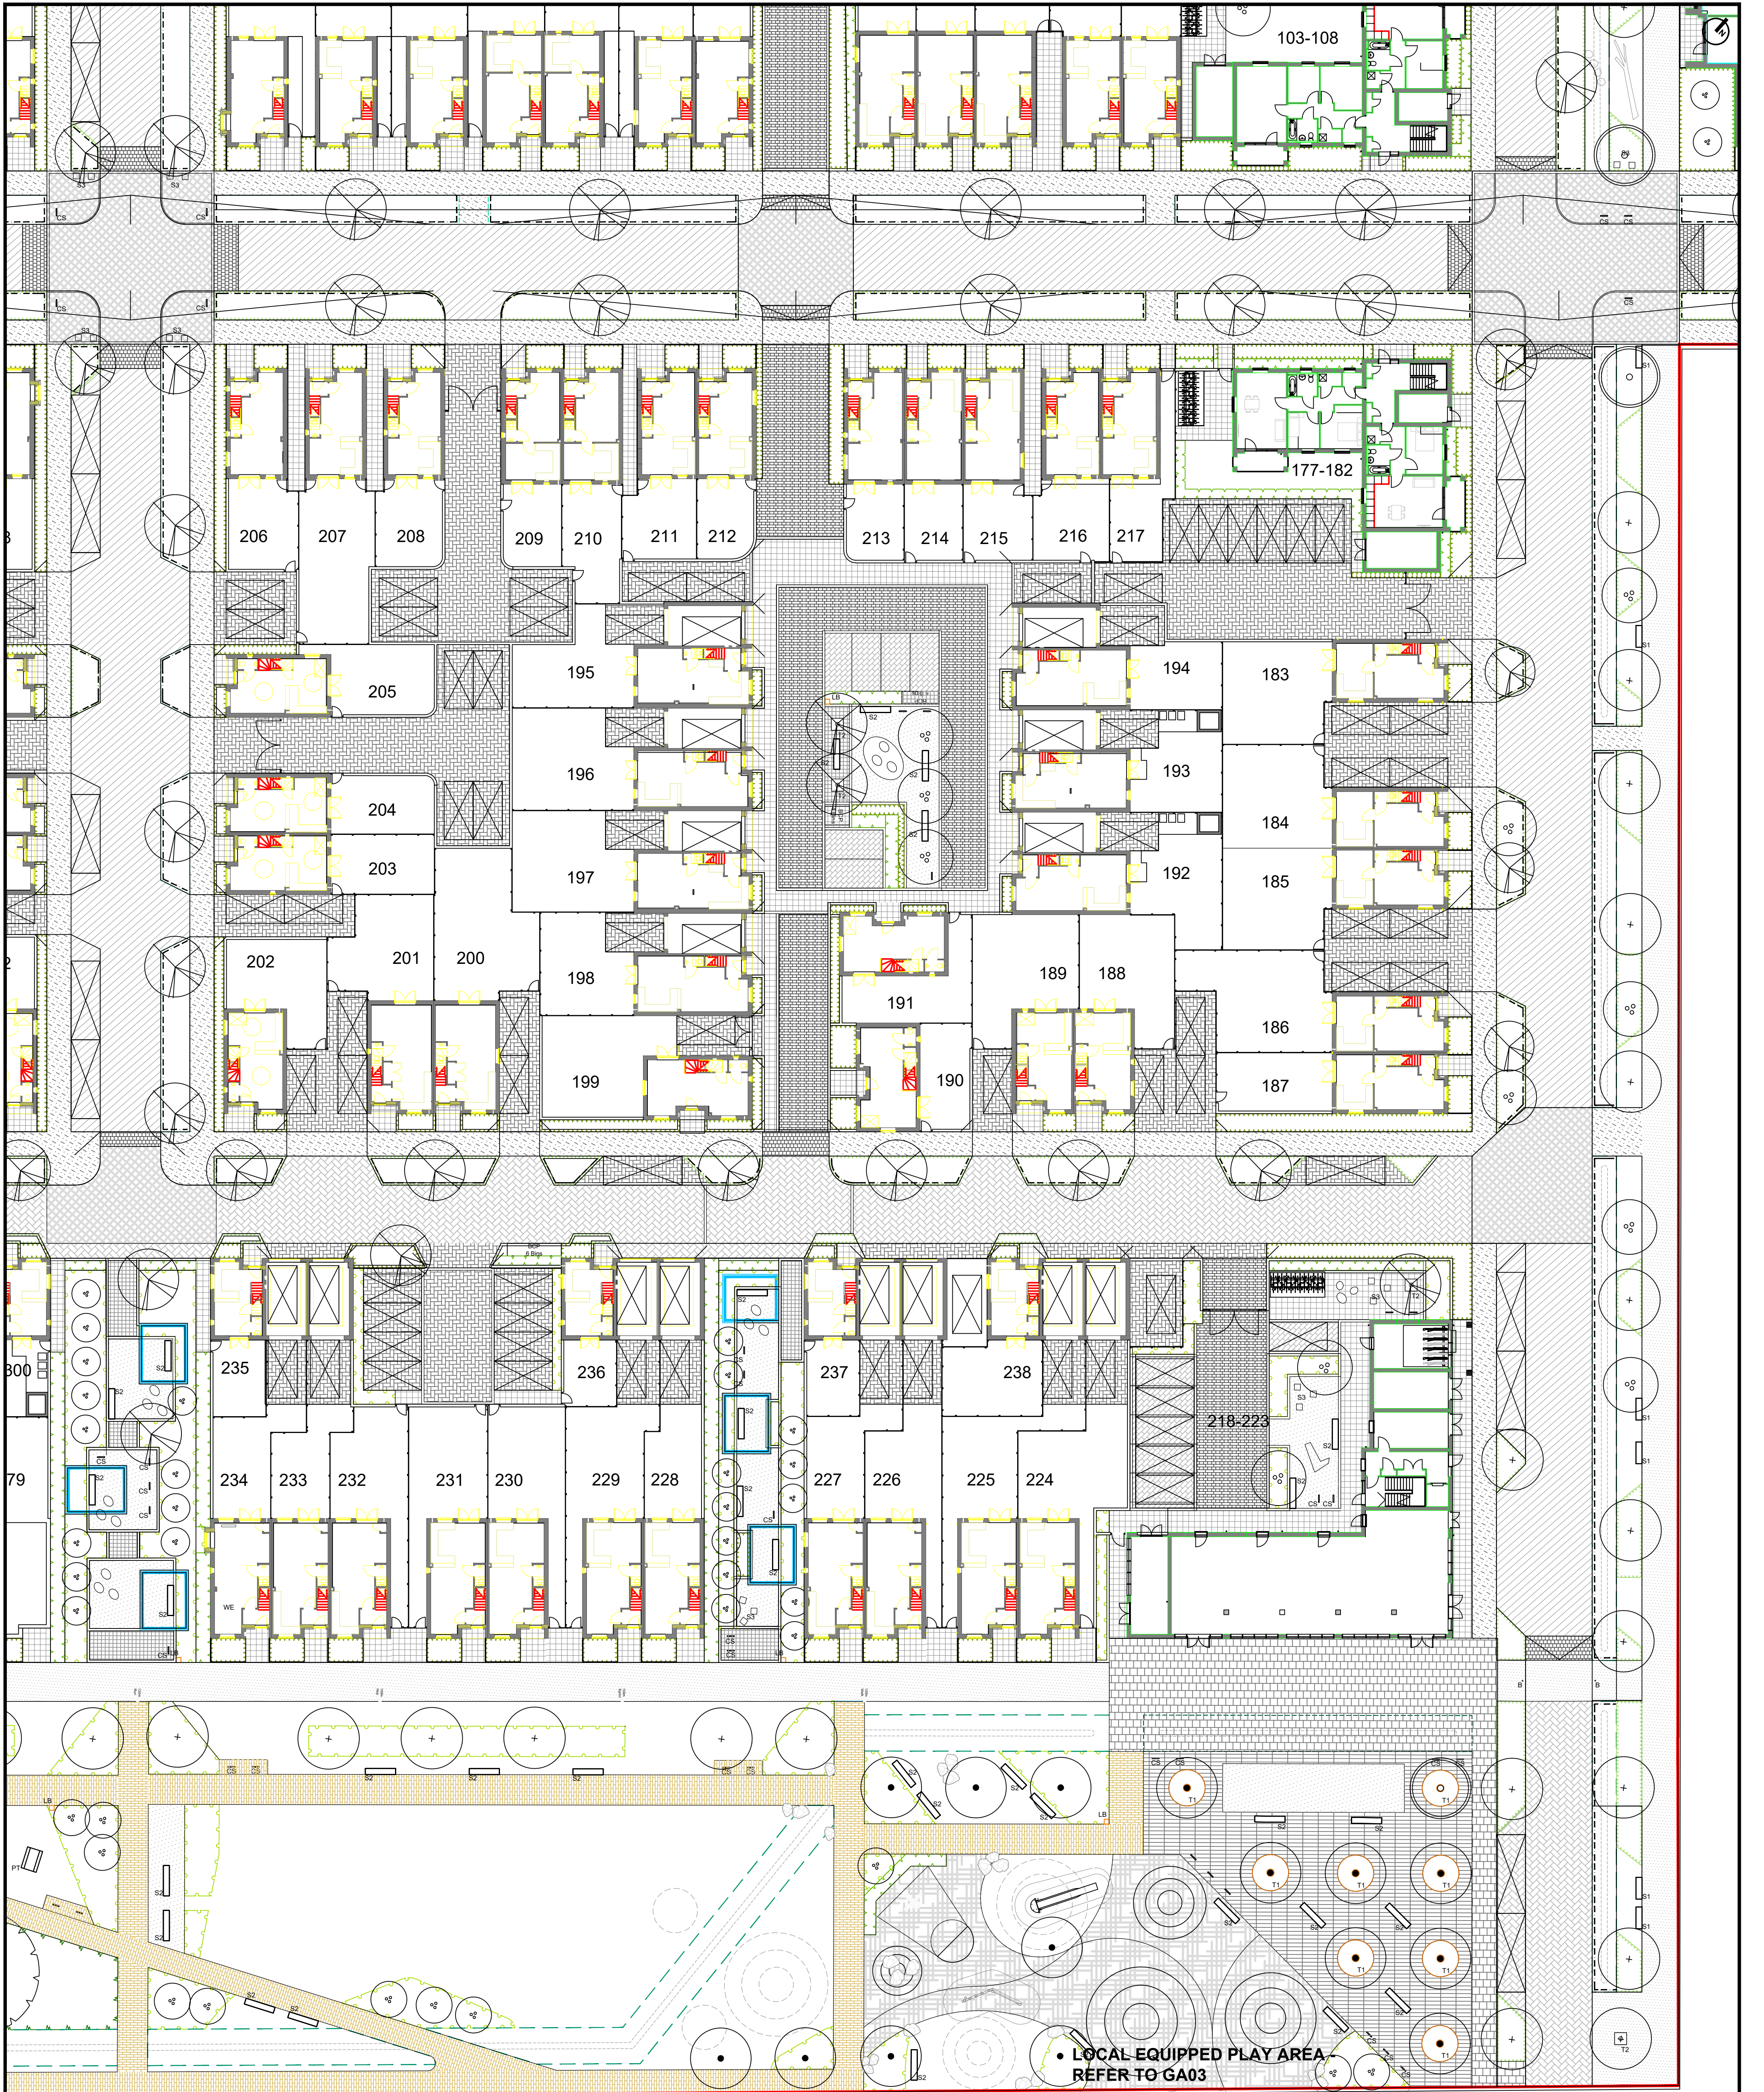

LEGEND

Application boundary

HARD LANDSCAPE

- Tarmac to roads
- Block paving laid in herringbone pattern to shared surface road (permeable where not adopted)
- Tarmac to pavements with standard concrete kerbs
- Permeable block paving laid in herringbone pattern to courtyard parking
- Permeable block paving laid in stretcher bond to courtyard parking
- Paving block to pedestrian areas within courtyards
- Block paving to shared surface within courtyards

Buff coloured concrete paving slabs to private access paths to houses

Bound gravel surfacing to courtyards

Block paving at key street junctions - to adoptable standards

Block paving ramps to raised tables

Buff coloured tarmac to cycle ways

Pathways in Greenway - bound gravel with block paved edging and banding to create panels

Feature paving to Town Park - York Stone or similar to meet Design Code requirements

Play safety surfacing in a variety of colours

Self bound gravel to Rampton Drift Greenway footpath

STREET FURNITURE

- Seating types 1 & 2 - benches with backs and arm rests
- Seating type 3 - single seating cubes
- Seating type 4 - curved bench to courtyard
- Picnic tables
- Incidental cycle racks - Stainless Steel Sheffield style stands within open spaces
- Tree grille type 1 - circular tree pit with steel edging and porous resin bound gravel finish
- Tree grille type 2 - square tree pit within paved area with steel edging and porous resin bound gravel finish
- Litter bin - to incorporate separate recycling and waste bins
- Concrete paving slabs to Town Park
- Timber raised planter to community garden
- Bollard
- Pergola structure within courtyards
- Circular pergola / gateway structure within community garden
- Incidental natural play / toddlers play features eg earth mounds, tree trunks, play boulders
- Themed play within safety surface - refer to GA03
- Knee rail or low bollards to edge of planting / swales along streets
- Railing and gates along front gardens
- Planting proposals - Refer to drawings PS01-05 for proposed tree species and planting strategy

KEY PLAN

Status FOR APPROVAL

ARC LANDSCAPE DESIGN AND PLANNING LTD.

Client

KEEPMOAT

Project

NORTHSTOWE - PHASE 2B

Drawing Title

GENERAL ARRANGEMENT HARDWORKS 5 OF 5

Scale

1:250@A1

Drawing Number

A307 GA05

Rev

Rev	Description	Date	By/Chk
D	Amendment to cycle storage and minor changes to layout	16-08-21	CS/VR
C	Minor amendments to layout	07-05-21	CS/VR
B	Minor amendments to Town Park	27-04-21	CS/VR
A	Minor amendments	16-04-21	CS/VR

Date

13/04/2021

Revision

D