



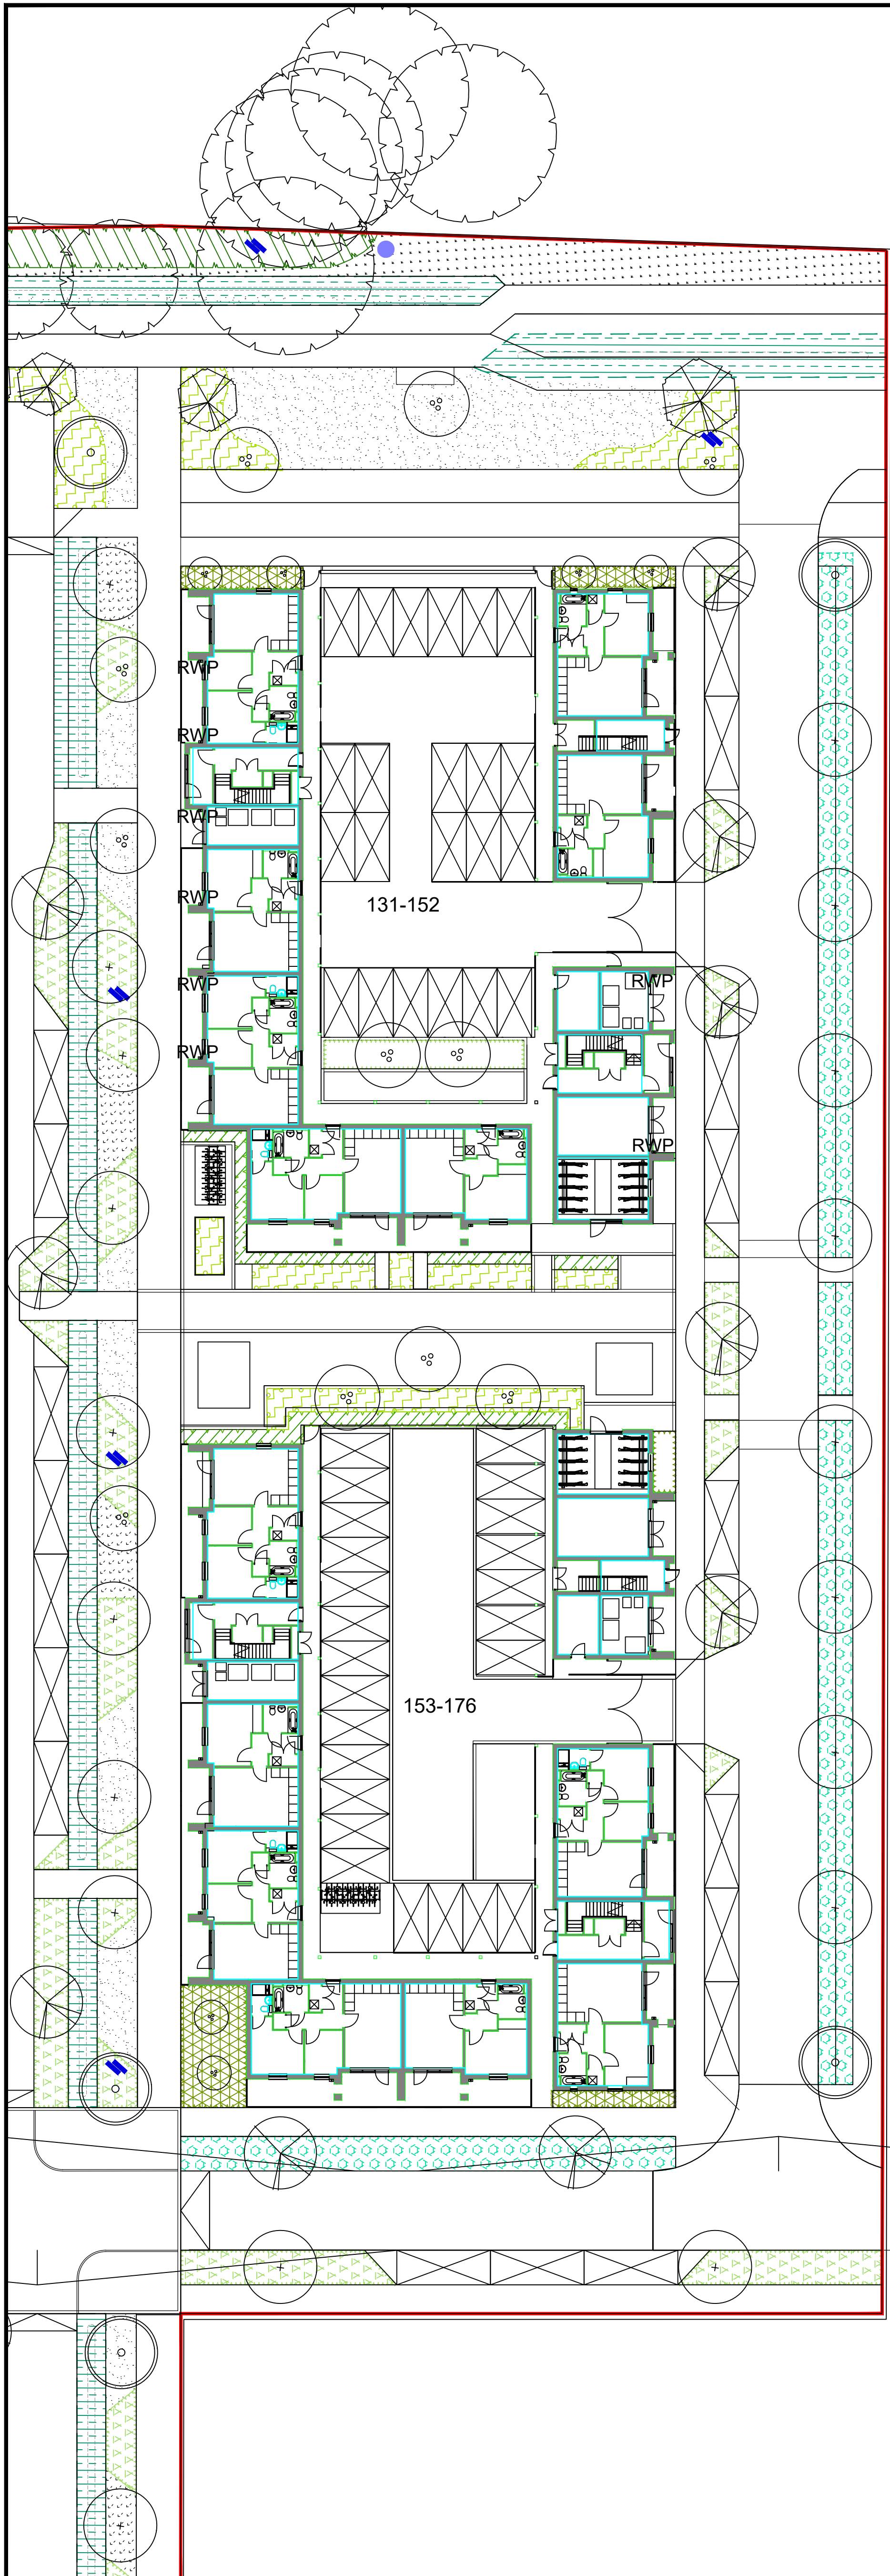

PLANT LIST

TREES

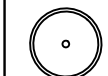

Feature trees:
Semi mature 6-7 m height
5-4x transplanted 30-35 cm girth

Species to include:
Betula nigra - River Birch
Catalpa bignonioides - Indian Bean Tree
Liquidambar styraciflua - Sweet Gum
Metasequoia glyptostroboides - Dawn Redwood



Avenue trees:
Semi mature 6-7 m height
4x transplanted 30-35 cm girth

Species to include:
Alnus glutinosa 'Laciniata' - Cut-leaf Alder
Corylus colurna - Turkish Hazel
Quercus robur 'Fastigiata' - Cypress Oak
Ulmus 'Lobel' - Elm



Street trees:
Semi mature 5-5.5 m height
3x transplanted 20-25 cm girth

Species to include:
Acer campestre 'Streetwise'
Acer rubrum 'Scanlon' - Red Maple
Prunus 'Sunset Boulevard' - Flowering Cherry
Pyrus calleryana 'Chanticleer' - Flowering Pear
Sorbus aucuparia - Rowan




Native species trees:
Semi mature 5-5.5 m height
3x transplanted 20-25 cm girth

Species to include:
Carpinus betulus - Hornbeam
Populus alba - White Poplar
Quercus robur - Common Oak
Sorbus aria - Whitebeam



Town park trees:
Semi mature 5-6 m height
3x transplanted 25-30 cm girth

Species to include:
Liriodendron tulipifera - Tulip Tree
Pinus sylvestris - Scots Pine
Quercus ilex - Holm Oak
Tilia cordata 'Winter Orange' - Small-leaved Lime

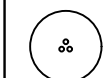

Multi-stem trees and specimen shrubs:
Mixed sizes:
3.5-4 m height, 4x transplanted
2.5-3 m height, 3x transplanted

Species to include:
Acer campestre - Field Maple
Amelanchier lamarckii - Juneberry
Cercidiphyllum japonicum - Katsura Tree
Pinus sylvestris - Scots Pine



Orchard trees:
1-2 m height transplants.
Species to be selected with specialist nursery advice to achieve satisfactory stock.

Local provenance and species that are known
Cambridgeshire varieties should be selected.
Varieties should all be domestic edible species with a mix of apples (not Cider), pear, cherry and hazelnut.


Refer to East of England Apples and Orchards
Project - www.applesandorchards.org.uk

Fruit trees to be planted in accordance with specialist
advice with open mesh tree guards.

PLANTING AREAS



Hedge planting:
Species to include:
Elaeagnus x ebbingei - Oleaster
Ligustrum ovalifolium 'Aureum' - Golden Privet
Osmanthus x burkwoodii - Osmanthus
Viburnum tinus - Laurustinus

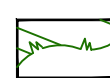

Native hedge planting:
Species to include:
Cornus sanguinea - Common Dogwood
Corylus avellana - Common Hazel
Crataegus monogyna - Hawthorn
Euonymus europaeus - Spindle
Prunus spinosa - Blackthorn
Lonitica periclymenum - Honeysuckle



Woodland foraging planting:
Species to include:
Allium ursinum - Wild Garlic
Fragaria vesca - Wild Strawberry
Malva sylvestris - Mallow
Corylus avellana - Hazel
Rumex acetosa - Common sorrel
Rumex acetosella - Sheep's sorrel
Vaccinium myrtillus - Blueberry
Lunaria annua - Honesty



Shrub planting to open spaces:
Shrub species to include:
Ceanothus 'Blue Mound' - Californian Lilac
Cornus alba - Red-barked Dogwood
Cornus sanguinea - Common Dogwood
Corylus avellana - Hazel
Escallonia 'Donard Star' - Escallonia
Garrya elliptica - Silk-tassel Bush
Hebe sp. - Shrubby Veronica
Lavandula angustifolia 'Munstead' - Lavender
Pittosporum 'Garnettii' - Pittosporum
Rosmarinus 'Miss Jessop' Upright' - Rosemary
Salvia officinalis 'Purpurascens' - Purple Sage
Syringa 'Madame Lemoine' - Lilac

Herbaceous species to include:
Geranium 'Rozanne' - Geranium
Iris sibirica - Siberian Iris
Miscanthus 'Kleine Fontane' - Chinese Silver Grass
Phlox russelliana - Turkish Sage
Stachys byzantina 'Silver Carpet' - Lambs' Ears




Low shrub planting to front of houses:
Shrub species to include:
Choisya 'Aztec Pearl' - Mexican Orange Blossom
Choisya ternata 'Sundance' - Mexican Orange Blossom
Eleagnus 'Gilt Edge' - Oleaster
Euonymus 'Emerald Gaiety' - Fortune's Spindle
Hebe sp. - Shrubby Veronica
Lavandula sp. - Lavender
Mahonia 'Apollo' - Oregon Grape
Osmanthus x burkwoodii - Osmanthus
Pittosporum sp. - Pittosporum
Philadelphus 'Manteau d'Hermine' - Mock Orange
Viburnum davidii - Viburnum

Herbaceous species to include:
Agapanthus 'White Heaven' - African Lily
Crocsmia 'Solfatara' - Monbretia
Dryopteris filix-mas - Male Fern
Hakonechloa macra 'Alboarea' - Golden Hakone Grass




Low shrub/ground cover planting to street:
Shrub species to include:
Euonymus 'Silver Queen' - Spindle
Hebe albicans - Shrubby Veronica
Hypericum x moserianum - Gold Flower
Lavandula 'Alba' - White Lavender
Lonitica nitida - Box Honeysuckle
Pittosporum 'Tom Thumb' - Pittosporum
Viburnum opulus 'Compactum' - Guelder Rose
Vinca minor 'Gertrude Jekyll' - Lesser White Periwinkle

Herbaceous species to include:
Kniphofia 'Brimstone' - Red-hot Poker
Helleborus x hybridus 'Harvington White' - Hellebore
Polystichum aculeatum - Hard Shield Fern
Stipa tenuifolia - Mexican Feather Grass

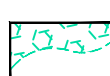


Rain garden planting:
Shrub species to include:
Cornus stolonifera 'Flaviramea' - Golden-twig Dogwood
Hydrangea arborescens 'Annabelle' - Hydrangea

Herbaceous species to include:
Acanthus mollis - Bear's Breeches
Deschampsia cespitosa - Tufted Hair Grass
Hemerocallis 'Golden Chimes' - Daylily
Rudbeckia fulgida - Black-eyed Susan

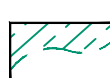


Swale planting:
Species to include:
Ajuga reptans 'Catlin's Giant' - Bugle
Carex pendula - Pendulous Sedge
Filipendula ulmaria - Meadowweet
Iris pseudacorus - Yellow Iris
Osmunda regalis - Royal Fern

or for adopted grass swales - Emorsgate Meadow Mix - EM8

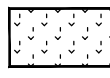

Proposed meadow / wildflower area
- Emorsgate Meadow Mix - EM4

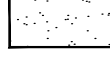

Proposed grassed areas -
Emorsgate EW1

Notes:

Outline Specification for Planting

All materials and installation to be undertaken in line with best horticultural practice and in accordance with guidance set out in British Standards specified relevant to this note and current at time of installation. All work to be carried out by horticultural trained personnel.

All composts, mulches and soil conditioners used in planting should be peat-free. The use of pesticides (herbicides, insecticides, fungicides and slug pellets) should be discouraged to prevent fatal effects on the food chain particularly invertebrates, birds and/or mammals. Any pesticides used should be non-residual.

All plants should be grown and sourced in the UK and should be supplied from a nursery approved in advance by the landscape architect. Any substitutes to be agreed prior to ordering.

Shrub and tree planting be undertaken when site and weather conditions are appropriate to successful establishment of plants and unless otherwise agreed in advance, to be undertaken between the months of 31st October and 31st March.
Turfing to occur in April-May or September-October subject to suitable weather conditions.

Soil additives to be introduced to all planting areas to include soil conditioner and slow release fertilizer to rates as specified by manufacturer.

Hedges to be planted in double staggered rows (unless otherwise specified) along either side of a timber post and 3 wire fence to aid establishment (unless adjacent to alternative boundary treatment).

A 300mm gravel strip is to be provided along building facades (not drawn). All plants to be set min 400mm from building/wall facades.

Once planted all areas must be kept adequately watered to ensure establishment and all areas must be kept weed and litter free at all times.

Soil Depths
All topsoil and subsoil used in planting areas to be accordance with British Standard BS3882:2015 and BS8545:2014, using the following recommended depths -

- Tree planting - 75mm mulch layer to 50cm radius from tree center for smaller trees in front gardens and 75cm radius to larger trees in open spaces. Mulch areas are to be kept free of grass during establishment. Trees to be planted in min. 400mm premium grade topsoil layer to upper level and 400mm free draining to lower level.
- Shrub planting - 50mm mulch layer, planted in min. 400mm premium grade topsoil layer.
- Grassed areas - min 200mm general purpose topsoil layer.

Soil analysis of all imported materials to be approved by the landscape architect in advance of purchase and delivery.

Proposed Trees

Growing space for all tree planting should be optimised, using tree pit trenches where possible. Each tree should have access to min. 5m² growing medium, where trenches are possible this should be considerably greater. Back filled with topsoil and subsoil as indicated above.

Trees within open spaces set within other soft landscaping area should have a tree pit 1.3m² wide by 0.80m deep. Back filled with topsoil and subsoil as indicated above.

The ground at the base of the tree pit should be broken up if ground is compacted or if there are apparent problems with drainage. Include 100mm of gravel to base of trench to aid free draining, subject to detail investigation of ground conditions. Where the ground conditions result in the base of the tree pits being compacted or not free draining, pits and trenches will require positive drainage to all trees to establish and thrive.

Project engineer to include low level lintels within boundary/garden walls to accommodate trees located next to walls.

Tree Support

All new tree planting to include provision for tree support to assist with the early years of establishment as follows:

All trees to front gardens to be single staked with 1.5m high, 75mm Ø round treated softwood stake. Stakes to be secured with adjustable bio-degradable rubber belt with spacers, secured approx. 100mm below the top of the stake.

All other trees to be double staked with 2no. 1.5m high, 75mm Ø round treated softwood stakes. Stakes to be secured with adjustable bio-degradable rubber cross bar with spacers, secured approx. 100mm below the top of the stake.
Orchard trees to include single stake with perforated tree guard.

Tree Irrigation and Aeration

All tree planting to include a tree irrigation and aeration system eg Green Blue Urban RootRain Civic with 80mm inlet with 60mm watering circuit and vented cap on retainer chain, or similar approved.

Root Barriers

Linear root barriers are to be installed in locations confirmed by the project engineer to protect services/surface treatments as required. Root barriers should be set min. 1.2m from the center of the trunk and set as close to the surface as possible. Linear root barriers, e.g. Green Blue Urban ReRoot 2000 Root barrier or similar approved, should be installed to the manufacturers guidance, using a min. 600mm depth root barrier.

Where root barriers are for the protection of services or below ground attenuation, the root barrier should extend 300mm lower than the invert level of services. For details of services and any specific requirements, refer to engineer's drawings.

Grassed Areas

All grassed areas to be turfed unless otherwise instructed to ensure establishment before occupation, to be turfed with Rolawn Medallion or similar approved, on a suitably prepared bed cleared of all materials exceeding 35mm in any one direction. Soil to receive a pre-turfing fertilizer.

Implementation Programme






Planting to be undertaken in the first available planting season following construction of the adjacent building.

LEGEND






SOFT LANDSCAPE

Existing trees and vegetation to be retained

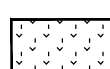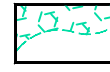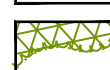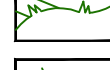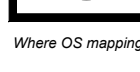


Visibility splays from driveways/
parking spaces - plants within
visibility splays to be <600mm height

BIODIVERSITY ENHANCEMENT

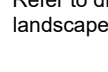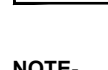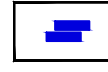

NOTE -
Refer to drawing GA01-05 for details on the hard
landscape strategy

KEY PLAN

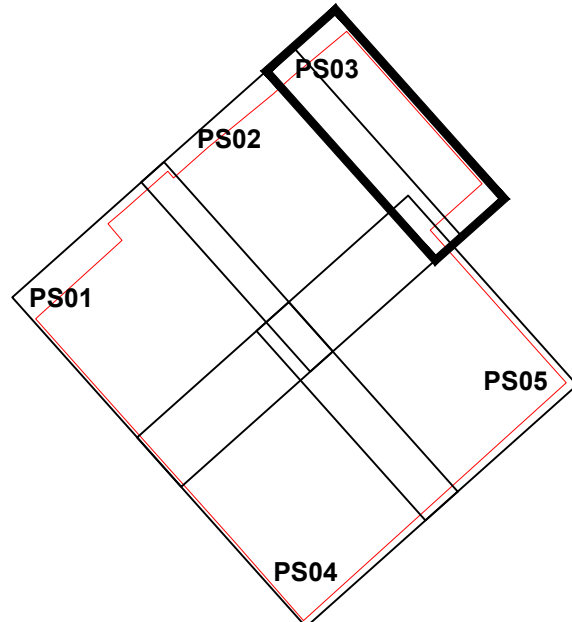

Rev Description Date By/Chk

E Amendment to cycle storage 16-08-21 CS/VR

D Minor amendments to layout 07/05/21 CS/VR

C Minor amendments to Town Park 27/04/21 CS/VR

B Amendment to layout 16/04/21 CS/VR

A Amendment to layout 13/04/21 CS/VR

Rev Description Date By/Chk

Rev Description Date By/Chk

Status FOR APPROVAL

ARC LANDSCAPE DESIGN AND PLANNING LTD.



Client

KEEPMOAT

Project

NORTHSTOWE - PHASE 2B

Drawing Title

PLANTING STRATEGY
3 OF 5

Scale

1:250@A1

Drawing Number

A307 PS03

By/Chk

CS/VR

Date

29/03/2021

Revision

E