


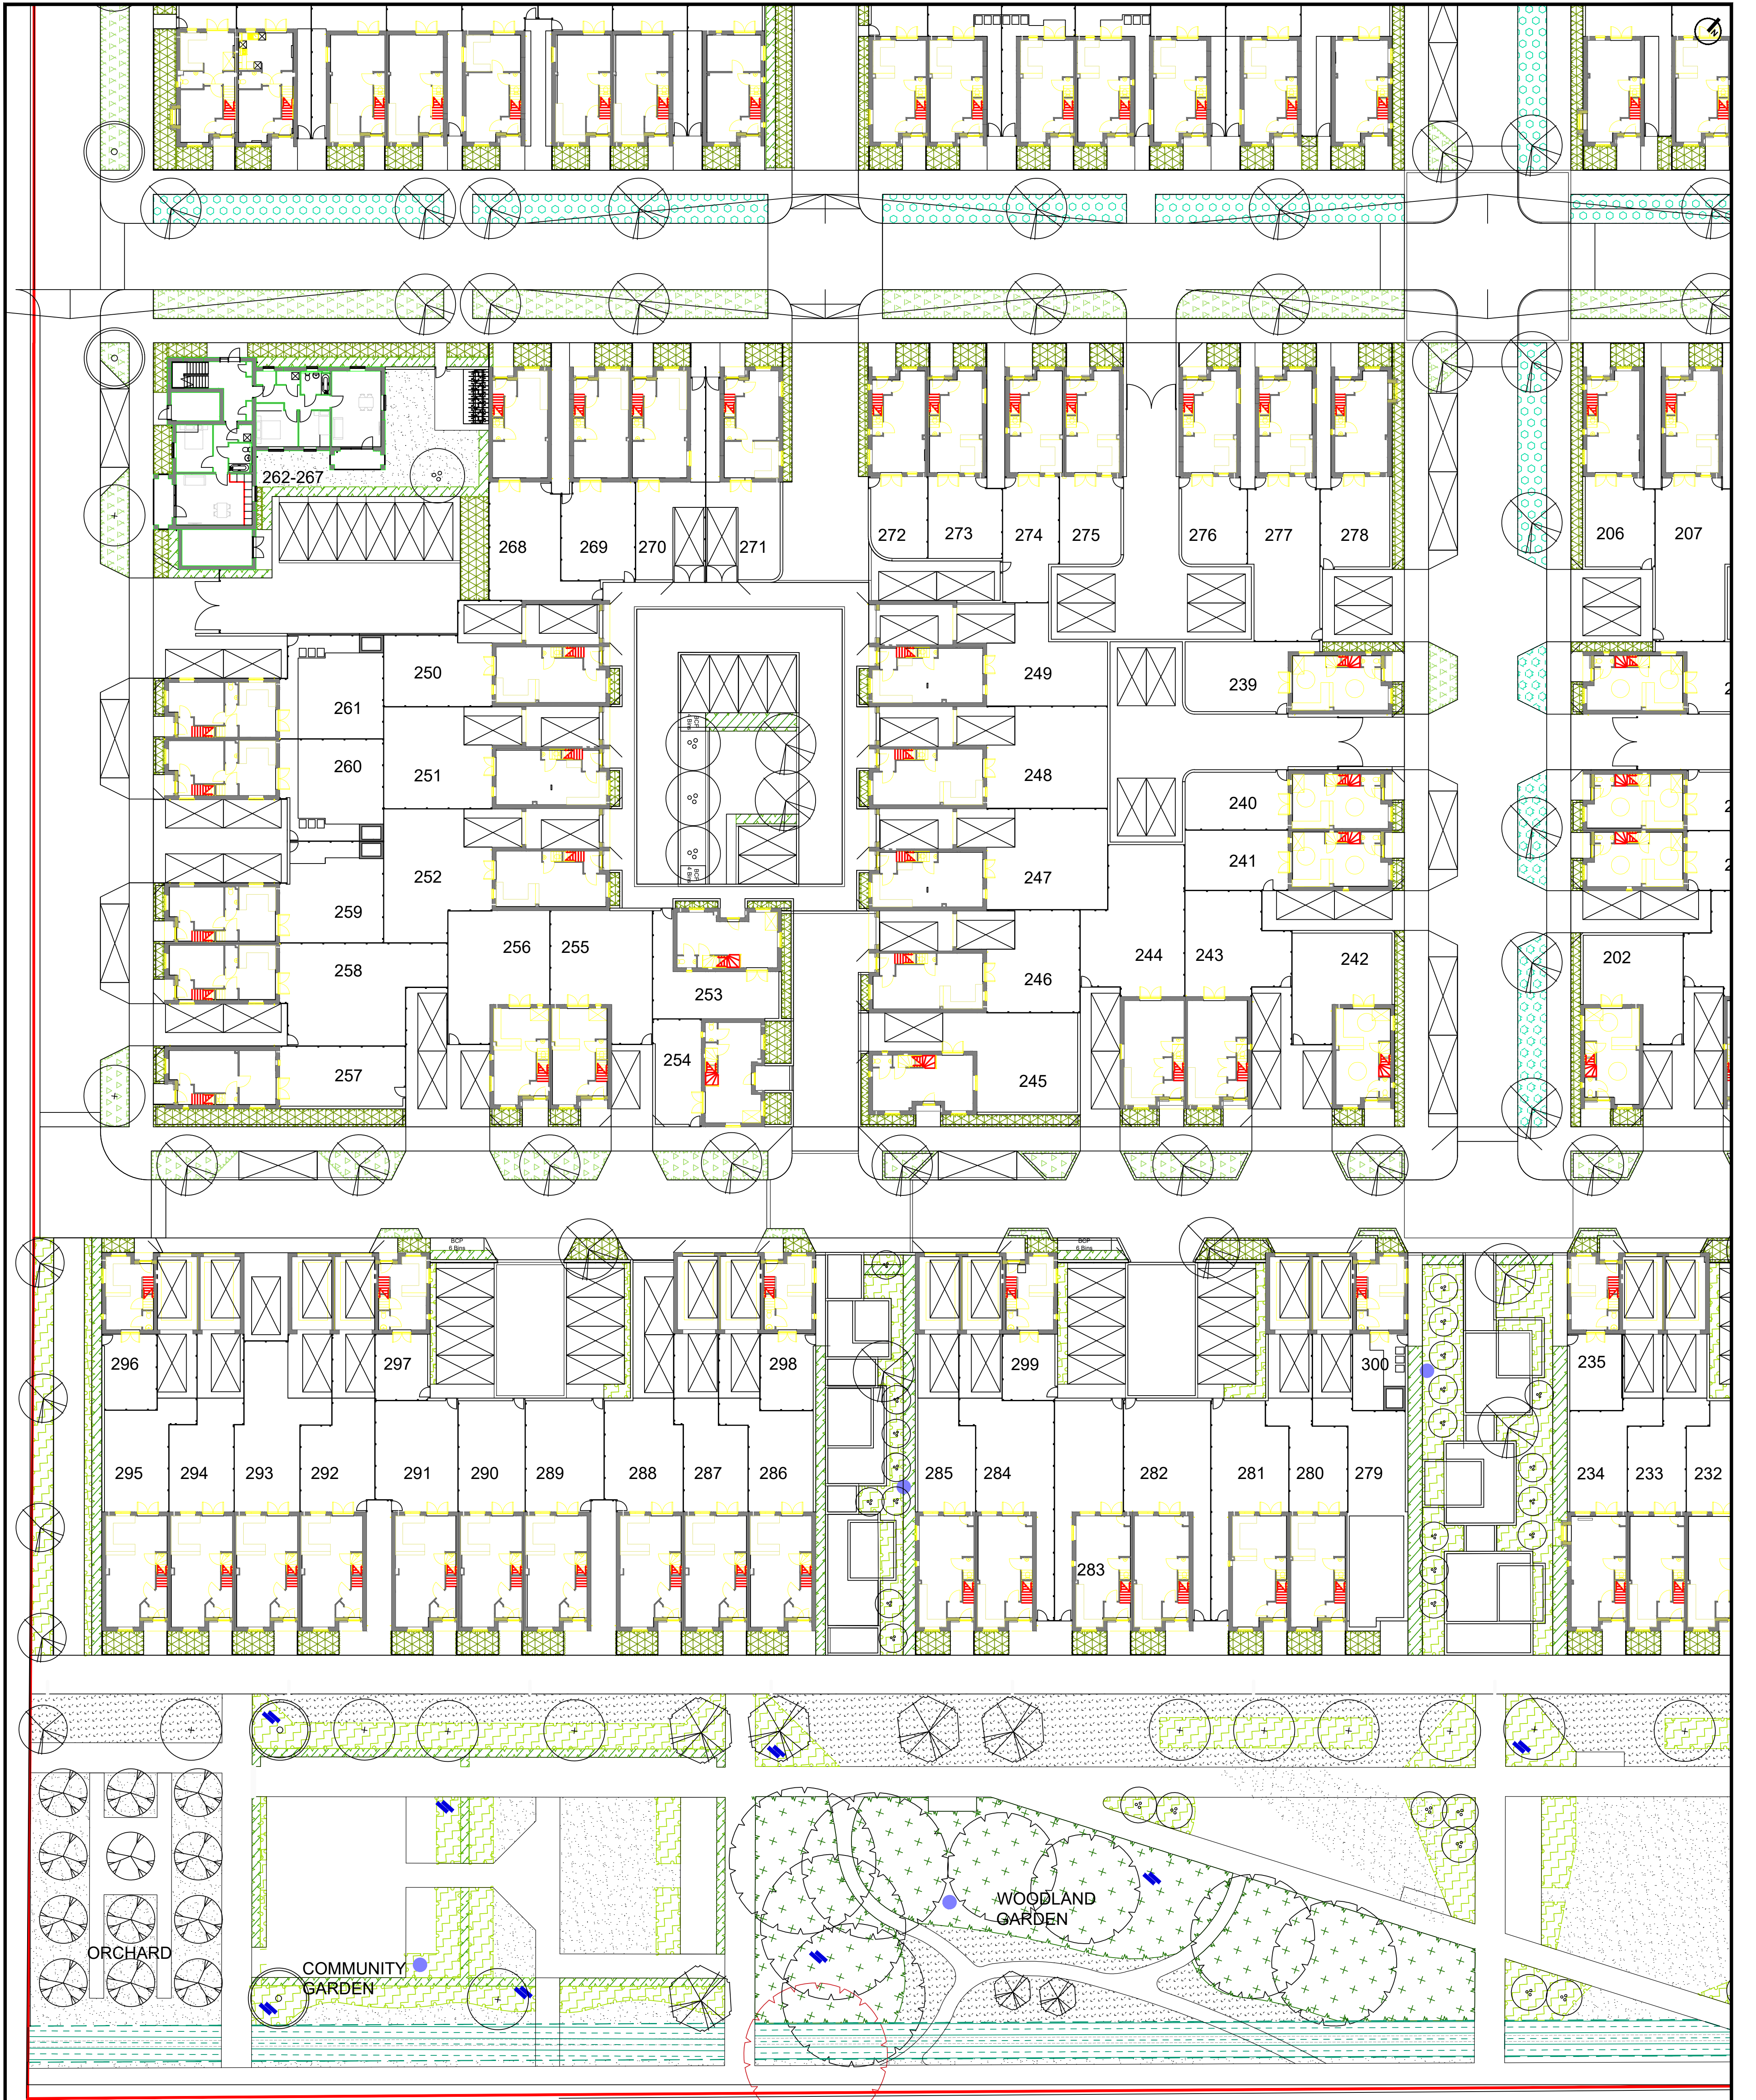

LEGEND

Application boundary

SOFT LANDSCAPE

Existing trees and vegetation to be retained

Feature trees

Avenue trees

Street trees

Native trees

Town park trees

Multi-stem tree and specimen shrub

Orchard trees

Hedge planting

Native hedge planting

Woodland foraging planting

Shrub planting to open spaces

Low shrub planting to front of houses

Rain garden planting

Low shrub/ground cover planting to street

Swale planting

Proposed meadow / wildflower area

Proposed grassed areas

Visibility splays from driveways/ parking spaces - plants within visibility splays to be <600mm height

BIODIVERSITY ENHANCEMENT

Bug hotel

Log pile/hibernacula

Bird box (detailed locations TBC with project ecologist)

Bat box (detailed locations TBC with project ecologist)

Swift box (detailed locations TBC with project ecologist)

NOTE-

Refer to drawing GA01-05 for details on the hard landscape strategy

Refer to drawing PS03 for detail on the planting and outline specification note

KEY PLAN

Rev

Rev	Description	Date	By/Chk
E	Amendment to cycle storage and minor changes to layout	16-08-21	CS/VR
D	Minor amendments to Layout	07/05/21	CS/VR
C	Minor amendments to Town Park	27/04/21	CS/VR
B	Amendment to layout	16/04/21	CS/VR
A	Amendment to layout	13/04/21	CS/VR

Scale

1:250@A1

Drawing Number

A307 PS04

Status FOR APPROVAL

ARC LANDSCAPE DESIGN AND PLANNING LTD.

Client

KEEPMOAT

Project

NORTHSTOWE - PHASE 2B

Drawing Title

PLANTING STRATEGY

4 OF 5

Scale

1:250@A1

Drawing Number

A307 PS04

Date

29/03/2021

Revision

E