



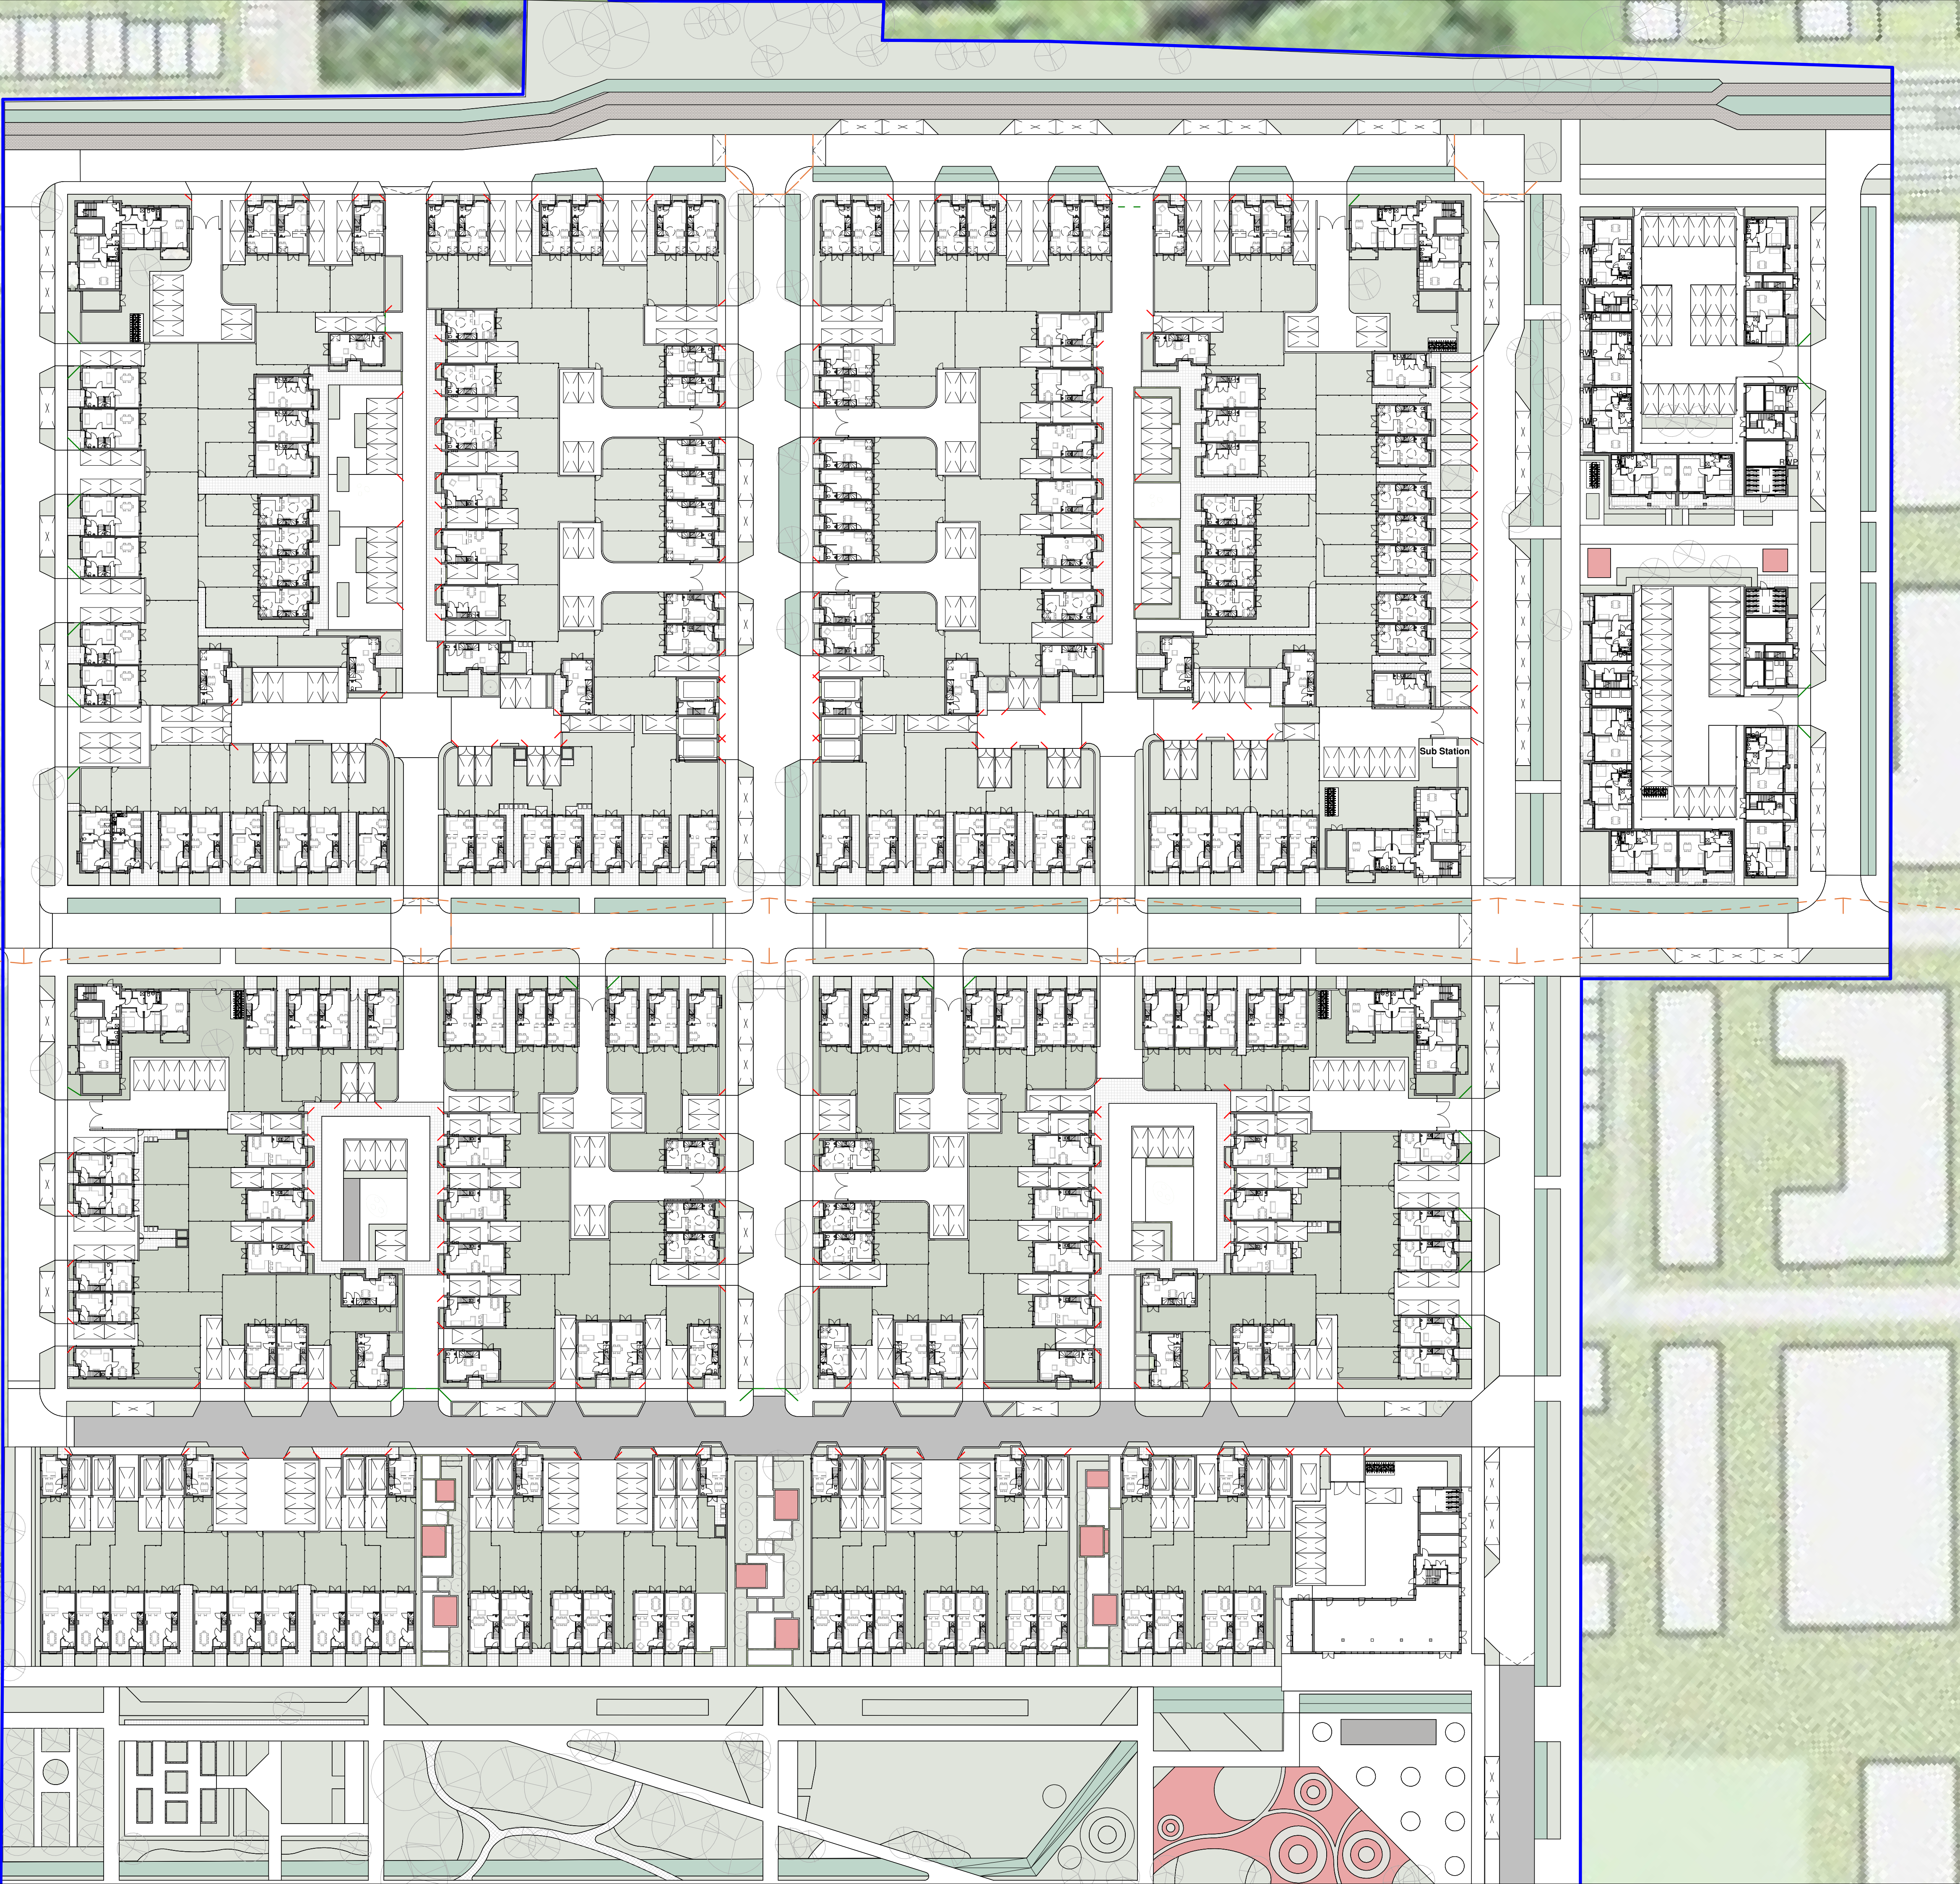

Legend

- Visibility Splays
- - - 1 X 1 Metre Visibility Splays
- - - 2 X 2 Metre Visibility Splays

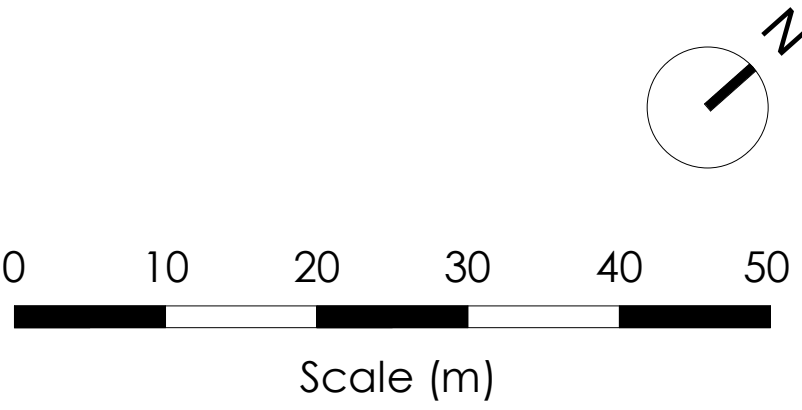

M	13/08/21	MDM	AB	Update bike stores, addition of 1.8m wall to back yard, Removal of green wall and replaced with 1.8m wall. Addition of 1.1m high railing around AB block. Update visibility splays. Update NE entry point
L	Date 34	MDM	AB	Relocation of Substation
K	03.08.21	MDM	AB	Added Visibility Splays
J	05.05.21	MM	TN	Updated to Homes England requirements
I	17.04.21	MM/KMac	AB	Updated Planning Issue
H	12.04.21	MM/KMac	AB	Planning Issue
G	07.04.21	KMac	AB	Site plan layout updated with new apartment block layout
F	24.03.21	KMac	AB	Design freeze layout issued
E	10.03.21	KMac	AB	Site layout updated as per comments
D	05.03.21	KMac	AB	Site layout updated as per comments
C	08.02.21	KMac	CJ	Site Layout updated for pre-app issue
B	01.02.21	KMac	CJ	Site Layout updated for pre-app issue
A	25.01.21	KMac	CJ	Site layout updated as per comments
rev	date	name	chk	note

boon brown

A Mowle, Alvington, Yeovil Somerset, BA20 2FG T 01932 420803 A Tintagel House, 92 Albert Embankment London, SE1 7TY T 0207 4989158 W www.boonbrown.com E info@boonbrown.com

A1

Original Sheet Size

STATUS

PLANNING

PROJECT
Northstowe Phase 2B

Northstowe (Oakington Barracks)
Cambridgeshire

CLIENT
Keepmoat Homes

DRAWING TITLE
Site Plan 1-500

SCALE	DATE	DRAWN	CHK
As indicated	03/23/21	KMac	AB
DRAWING NUMBER	4080- BBA - SP - 00 - DR - A - 1001		REVISION
			M

